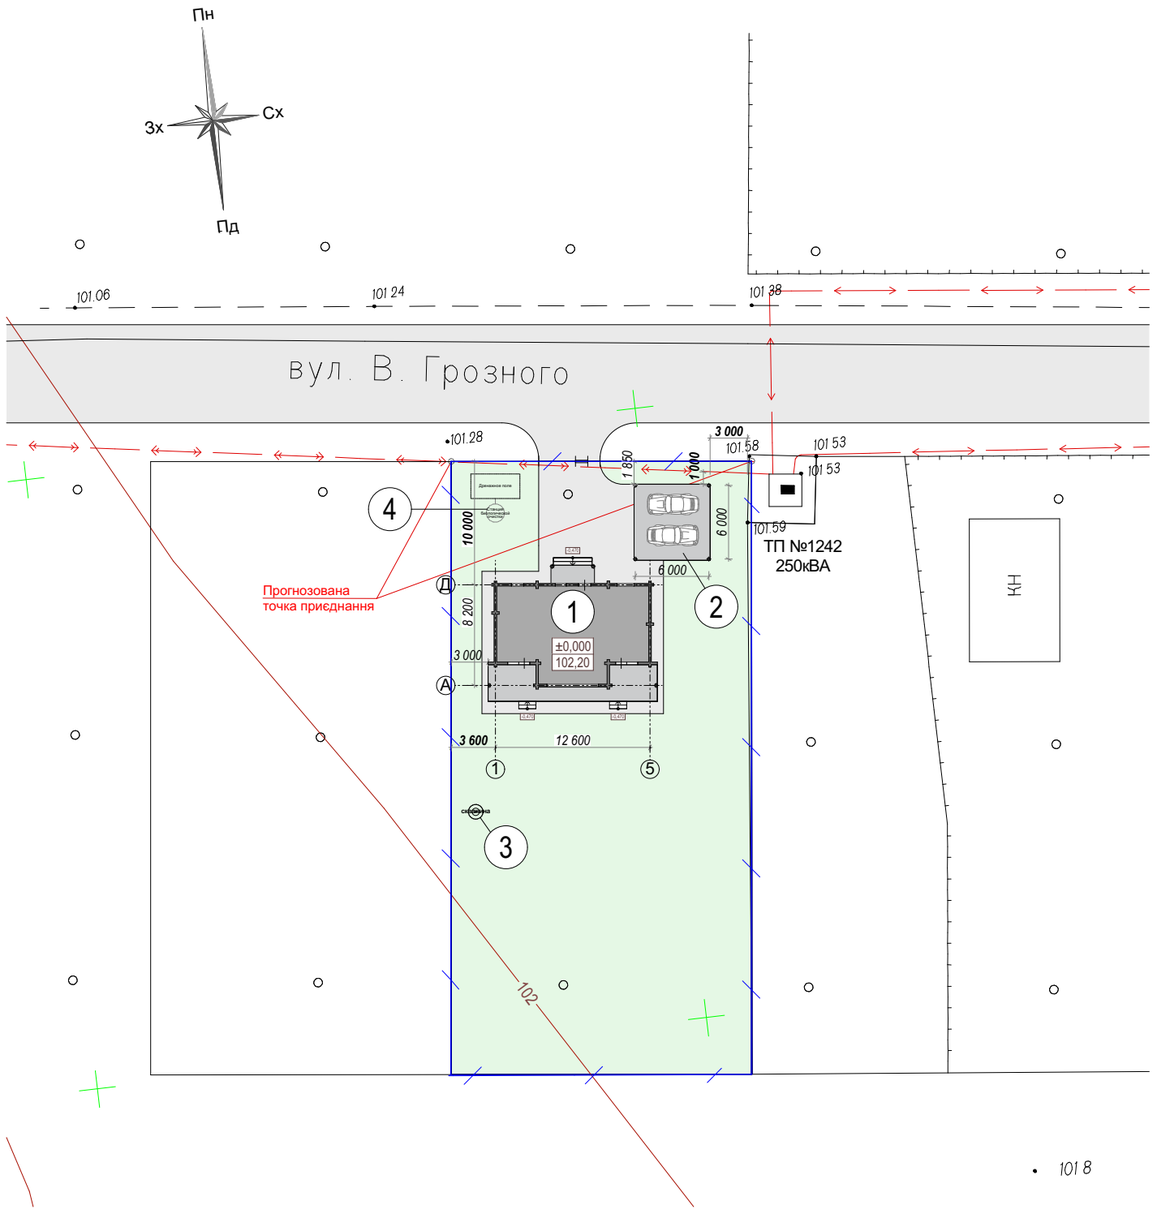

Экспликация зданий и сооружений

Номер на плане	Наименование	Этажность	Площадь застройки, м²	Координаты квадрата сетки
1	Проектируемый жилой дом	1 +мансарда	134,33	
2	Автонавес		38,44	
3	Скважина			
4	Септик			

Баланс территории

№ п/п	Наименование	Ед. изм.	Показатель	Баланс,%
1	Площадь участка	га	0,1224	100
2	Площадь застройки	м.кв.	172,77	14,1
3	Площадь мощения	м.кв.	104,72	8,6
4	Площадь озеленения	м.кв.	946,51	77,3
5	Плотность застройки	%	14,1	

Ведомость зданий и сооружений

Номер на плане	Наименование и отметка	Этажность	Количество			Площадь, м²				Строительный объем, м³	
			Зданий	Квартир		Застройки		Общая нормируемая		Здания	Всего
				Здания	Всего	Здания	Всего	Здания	Всего		
1	Жилой дом (102,20)	1 +мансарда	1			134,33	134,33	115,49	115,49	438,6	438,6

Примечания:

1. За условную отметку 0.000 жилого дома принят уровень чистого пола первого этажа, равной абсолютной отметке 102.20

Проектируемый жилой дом

Граница землепользования

Согласовано:

Взам. инв. №

Подп. и дата

Инв. № подл.

Изм.	Кол.уч.	Лист	№ док.	Подп.	Дата
ГАП		Морковник			11.19
Разраб.		Морковник			11.19
Проверил		Глушков			11.19

191114/1-01 - АР

Индивидуальный жилой дом, кадастровый номер участка – 3221884001:32:035:6022;
с. Лебедевка, Вышгородский р-н, Киевская область

Жилой дом

Стадия	Лист	Листов
ЕП	4	

Схема генерального плана

Копировал

М 1:500

Формат А3